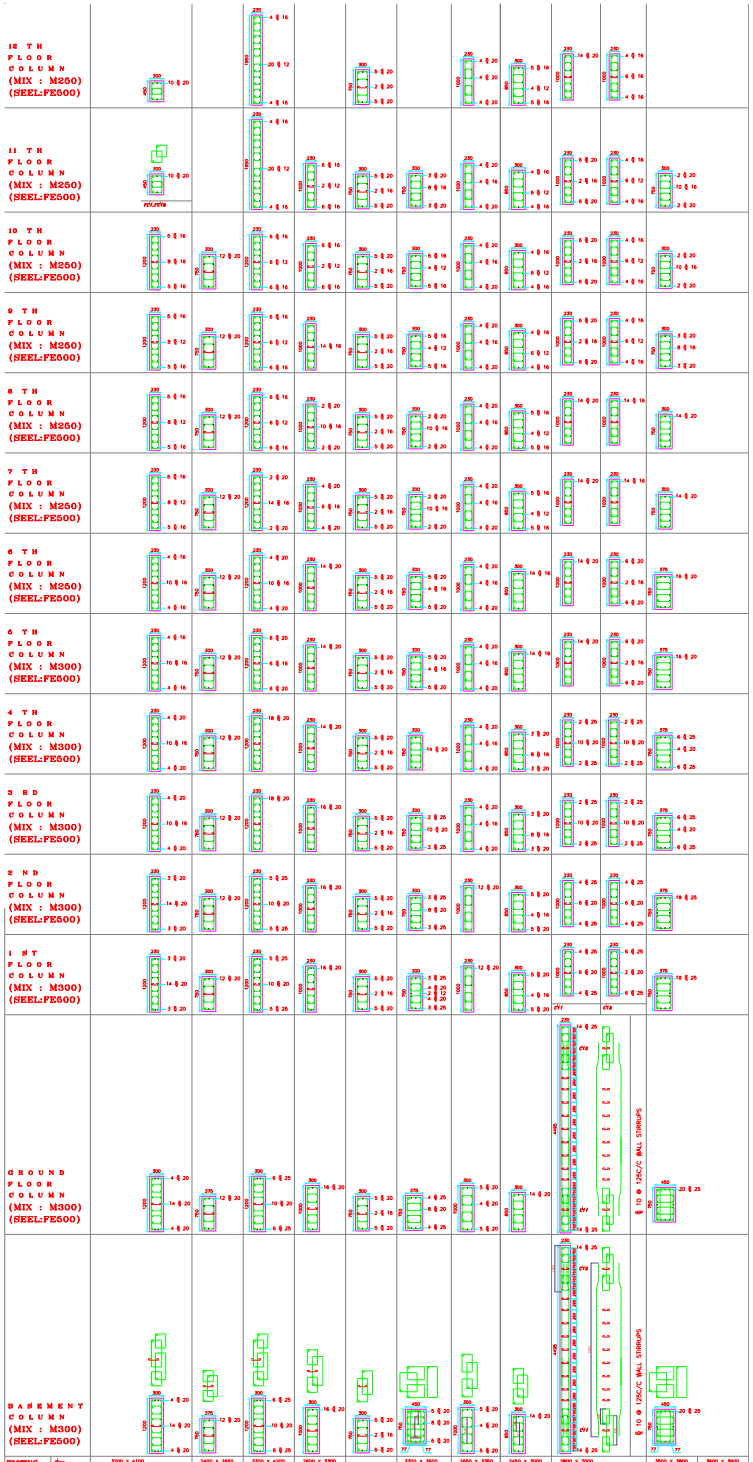
12 TH FLOOR COLUMN (MIX : M250) (SEEL:FE500)
11 TH FLOOR COLUMN (MIX : M250) (SEEL:FE500)
10 TH FLOOR COLUMN (MIX : M250) (SEEL:FE500)
9 TH FLOOR COLUMN (MIX : M250) (SEEL:FE500)
8 TH FLOOR COLUMN (MIX : M250) (SEEL:FE500)
7 TH FLOOR COLUMN (MIX : M250) (SEEL:FE500)
6 TH FLOOR COLUMN (MIX : M250) (SEEL:FE500)
5 TH FLOOR COLUMN (MIX : M300) (SEEL:FE500)
4 TH FLOOR COLUMN (MIX : M300) (SEEL:FE500)
3 RD FLOOR COLUMN (MIX : M300) (SEEL:FE500)
2 ND FLOOR COLUMN (MIX : M300) (SEEL:FE500)
1 ST FLOOR COLUMN (MIX : M300) (SEEL:FE500)
GROUND FLOOR COLUMN (MIX : M300) (SEEL:FE500)
BASEMENT COLUMN (MIX : M300) (SEEL:FE500)
@ 10 @ 125C/C BALL STIRRUPS
FOOTING DETAILS (MIX : M300) (SEEL : FE500)
Size
B W d
Short Span
Long Span
COLUMN MARK ( B-C-12 )
3200 X 4100
2400 X 2650
3300 X 4200
2600 X 3300
3350 X 3650
2950 X 3350
2450 X 3000
2900 X 7000
3500 X 3800
3600 X 3900
1100 TO 300
750 TO 230
1100 TO 300
900 TO 230
800 TO 230
1000 TO 300
900 TO 230
800 TO 230
1100 TO 300
1100 TO 300
@ 16 @ 130C/C
@ 12 @ 100C/C
@ 16 @ 100C/C
@ 12 @ 100C/C
@ 16 @ 100C/C
@ 16 @ 100C/C
@ 16 @ 150C/C
@ 16 @ 165C/C
@ 16 @ 175C/C
@ 16 @ 115C/C
@ 16 @ 100C/C
C12,C13
C8,C9
C8,C17
C12,C14
C5
C11,C19
C6
C10
C11,C18
C16
C16