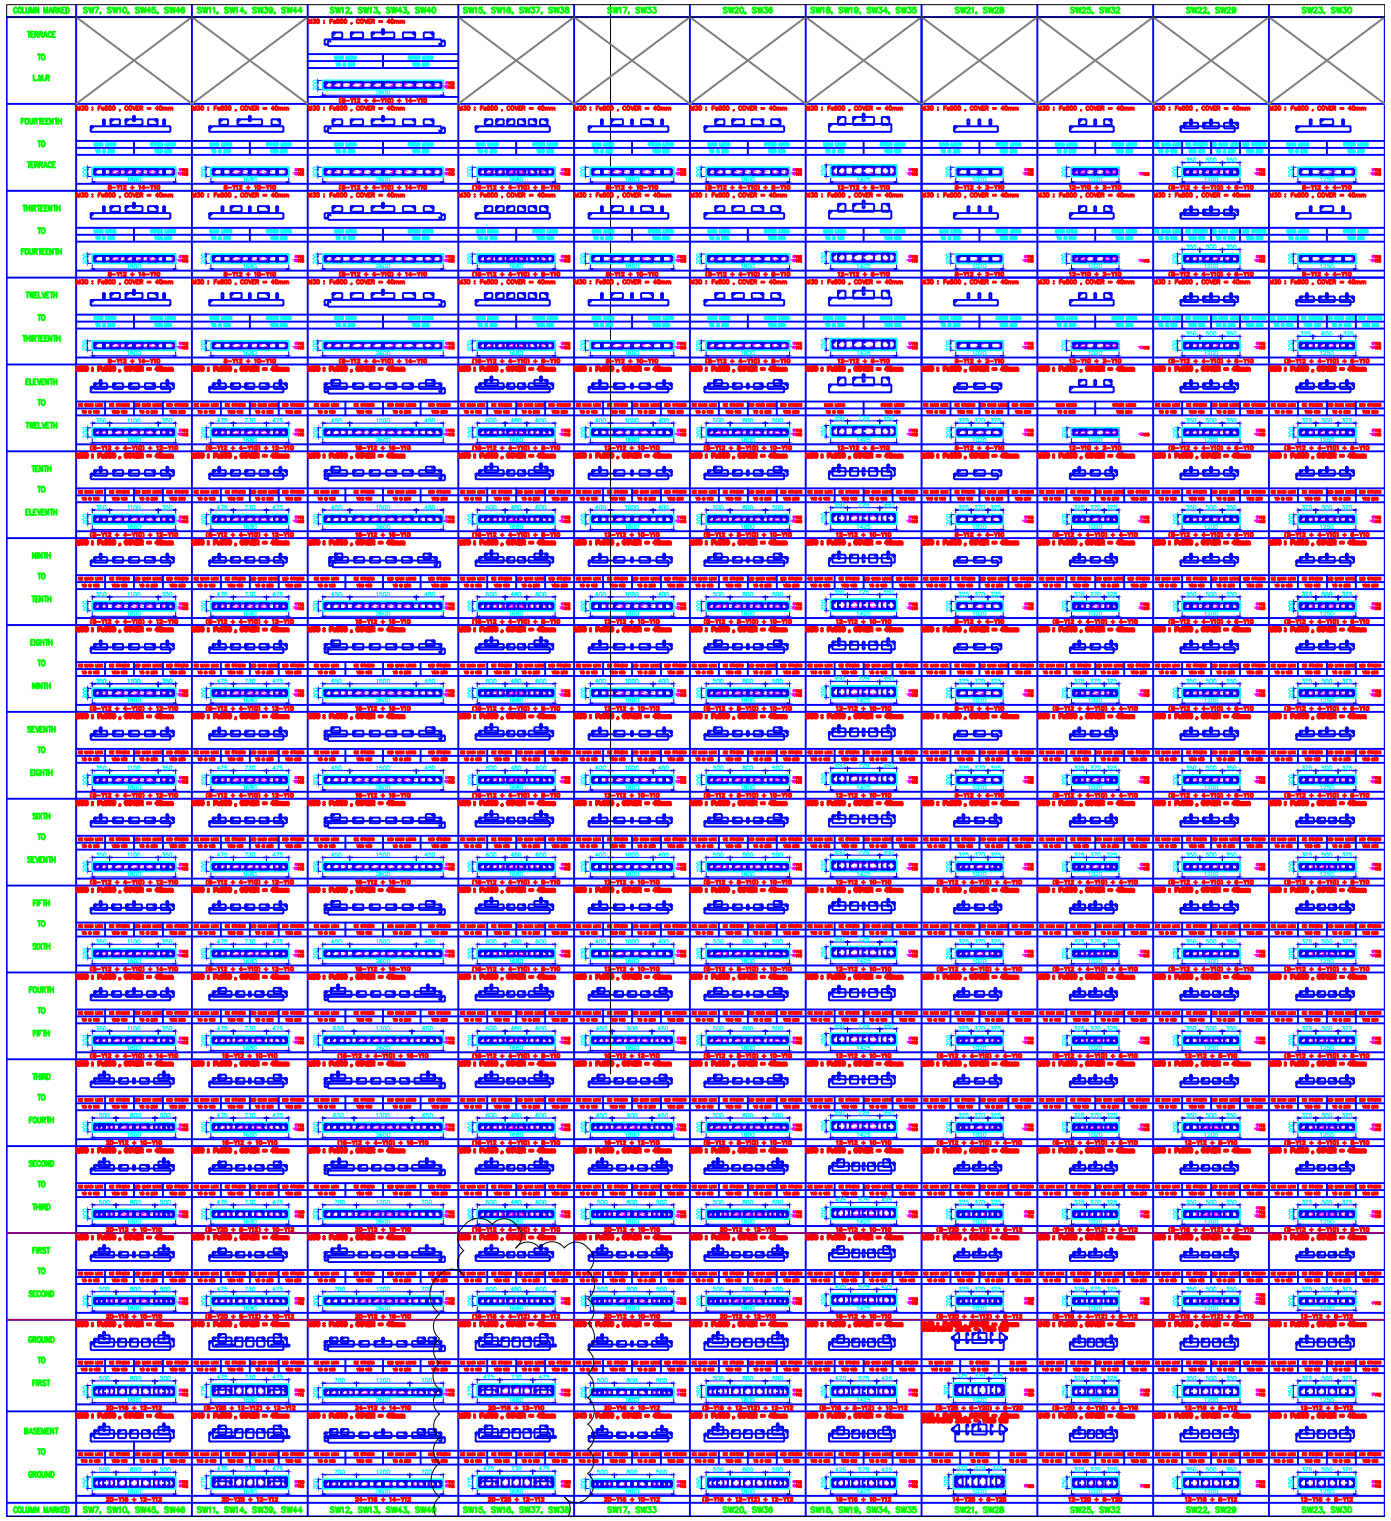
COLUMN MARKED
SW7, SW10, SW45, SW46
SW11, SW14, SW39, SW44
SW12, SW13, SW43, SW40
SW15, SW16, SW37, SW38
SW17, SW33
SW20, SW36
SW18, SW19, SW34, SW35
SW21, SW28
SW25, SW32
SW22, SW29
SW23, SW30
TERRACE TO L.M.R
FOURTEENTH TO TERRACE
THIRTEENTH TO FOURTEENTH
TWELVETH TO THIRTEENTH
ELEVENTH TO TWELVETH
TENTH TO ELEVENTH
NINTH TO TENTH
EIGHTH TO NINTH
SEVENTH TO EIGHTH
SIXTH TO SEVENTH
FIFTH TO SIXTH
FOURTH TO FIFTH
THIRD TO FOURTH
SECOND TO THIRD
FIRST TO SECOND
GROUND TO FIRST
BASEMENT TO GROUND
M30 : Fe500 , COVER = 40mm